
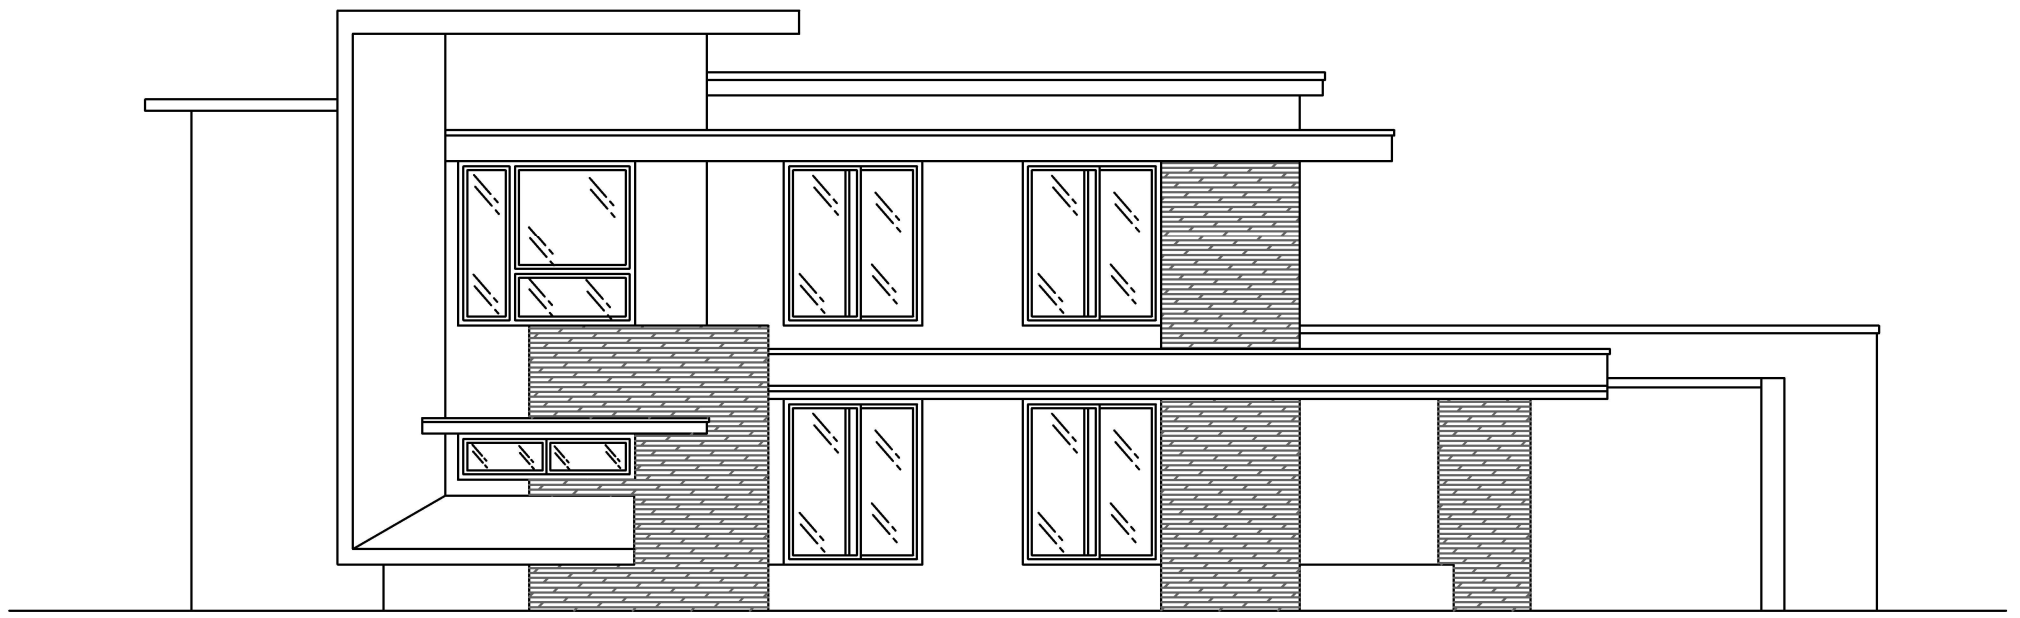
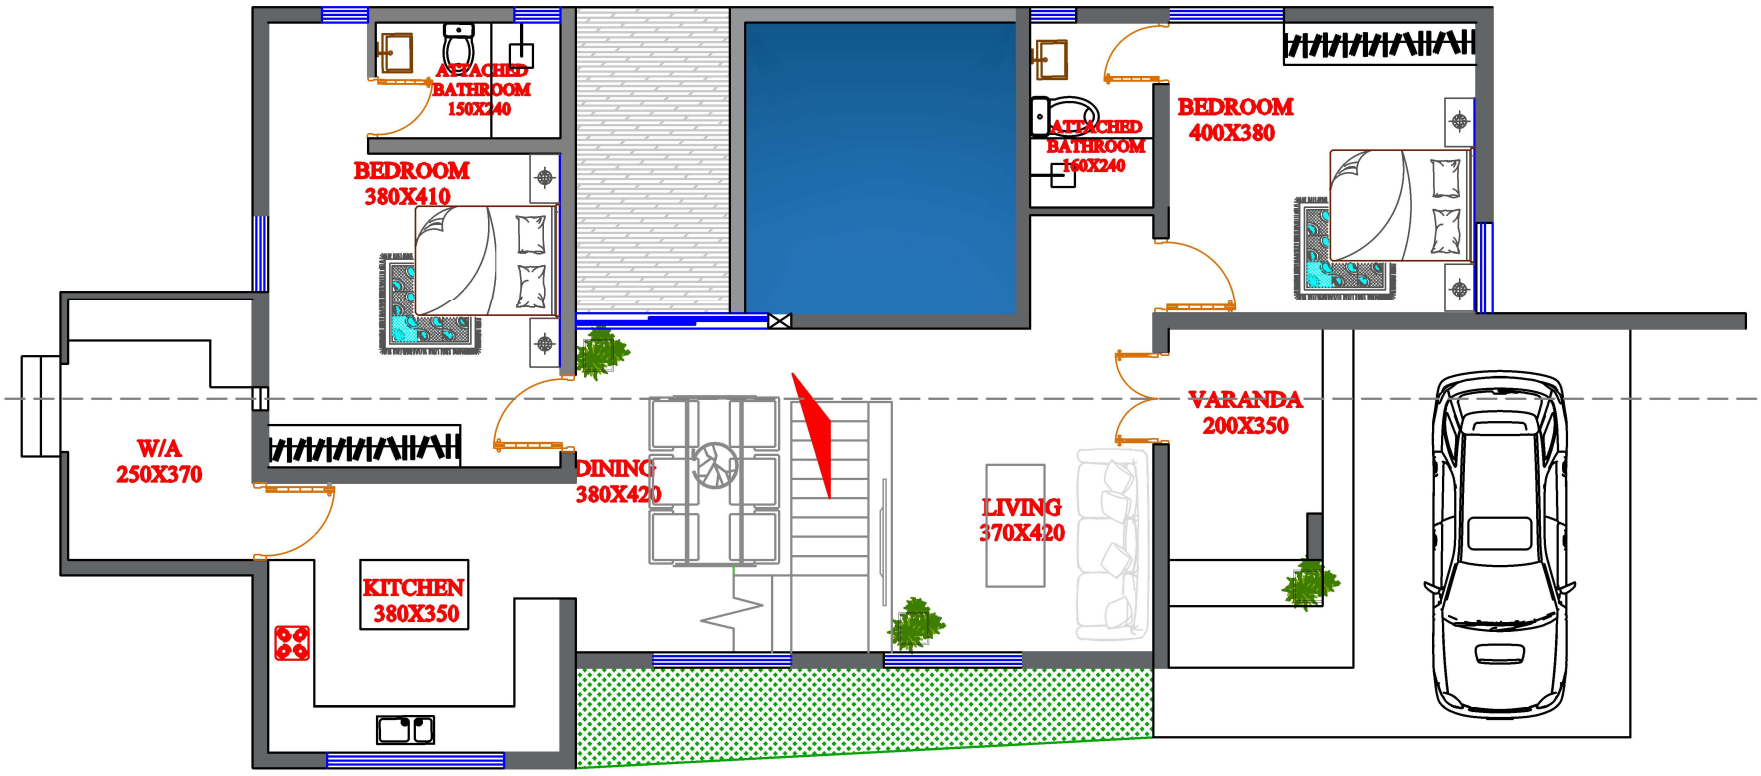



ELEVATION

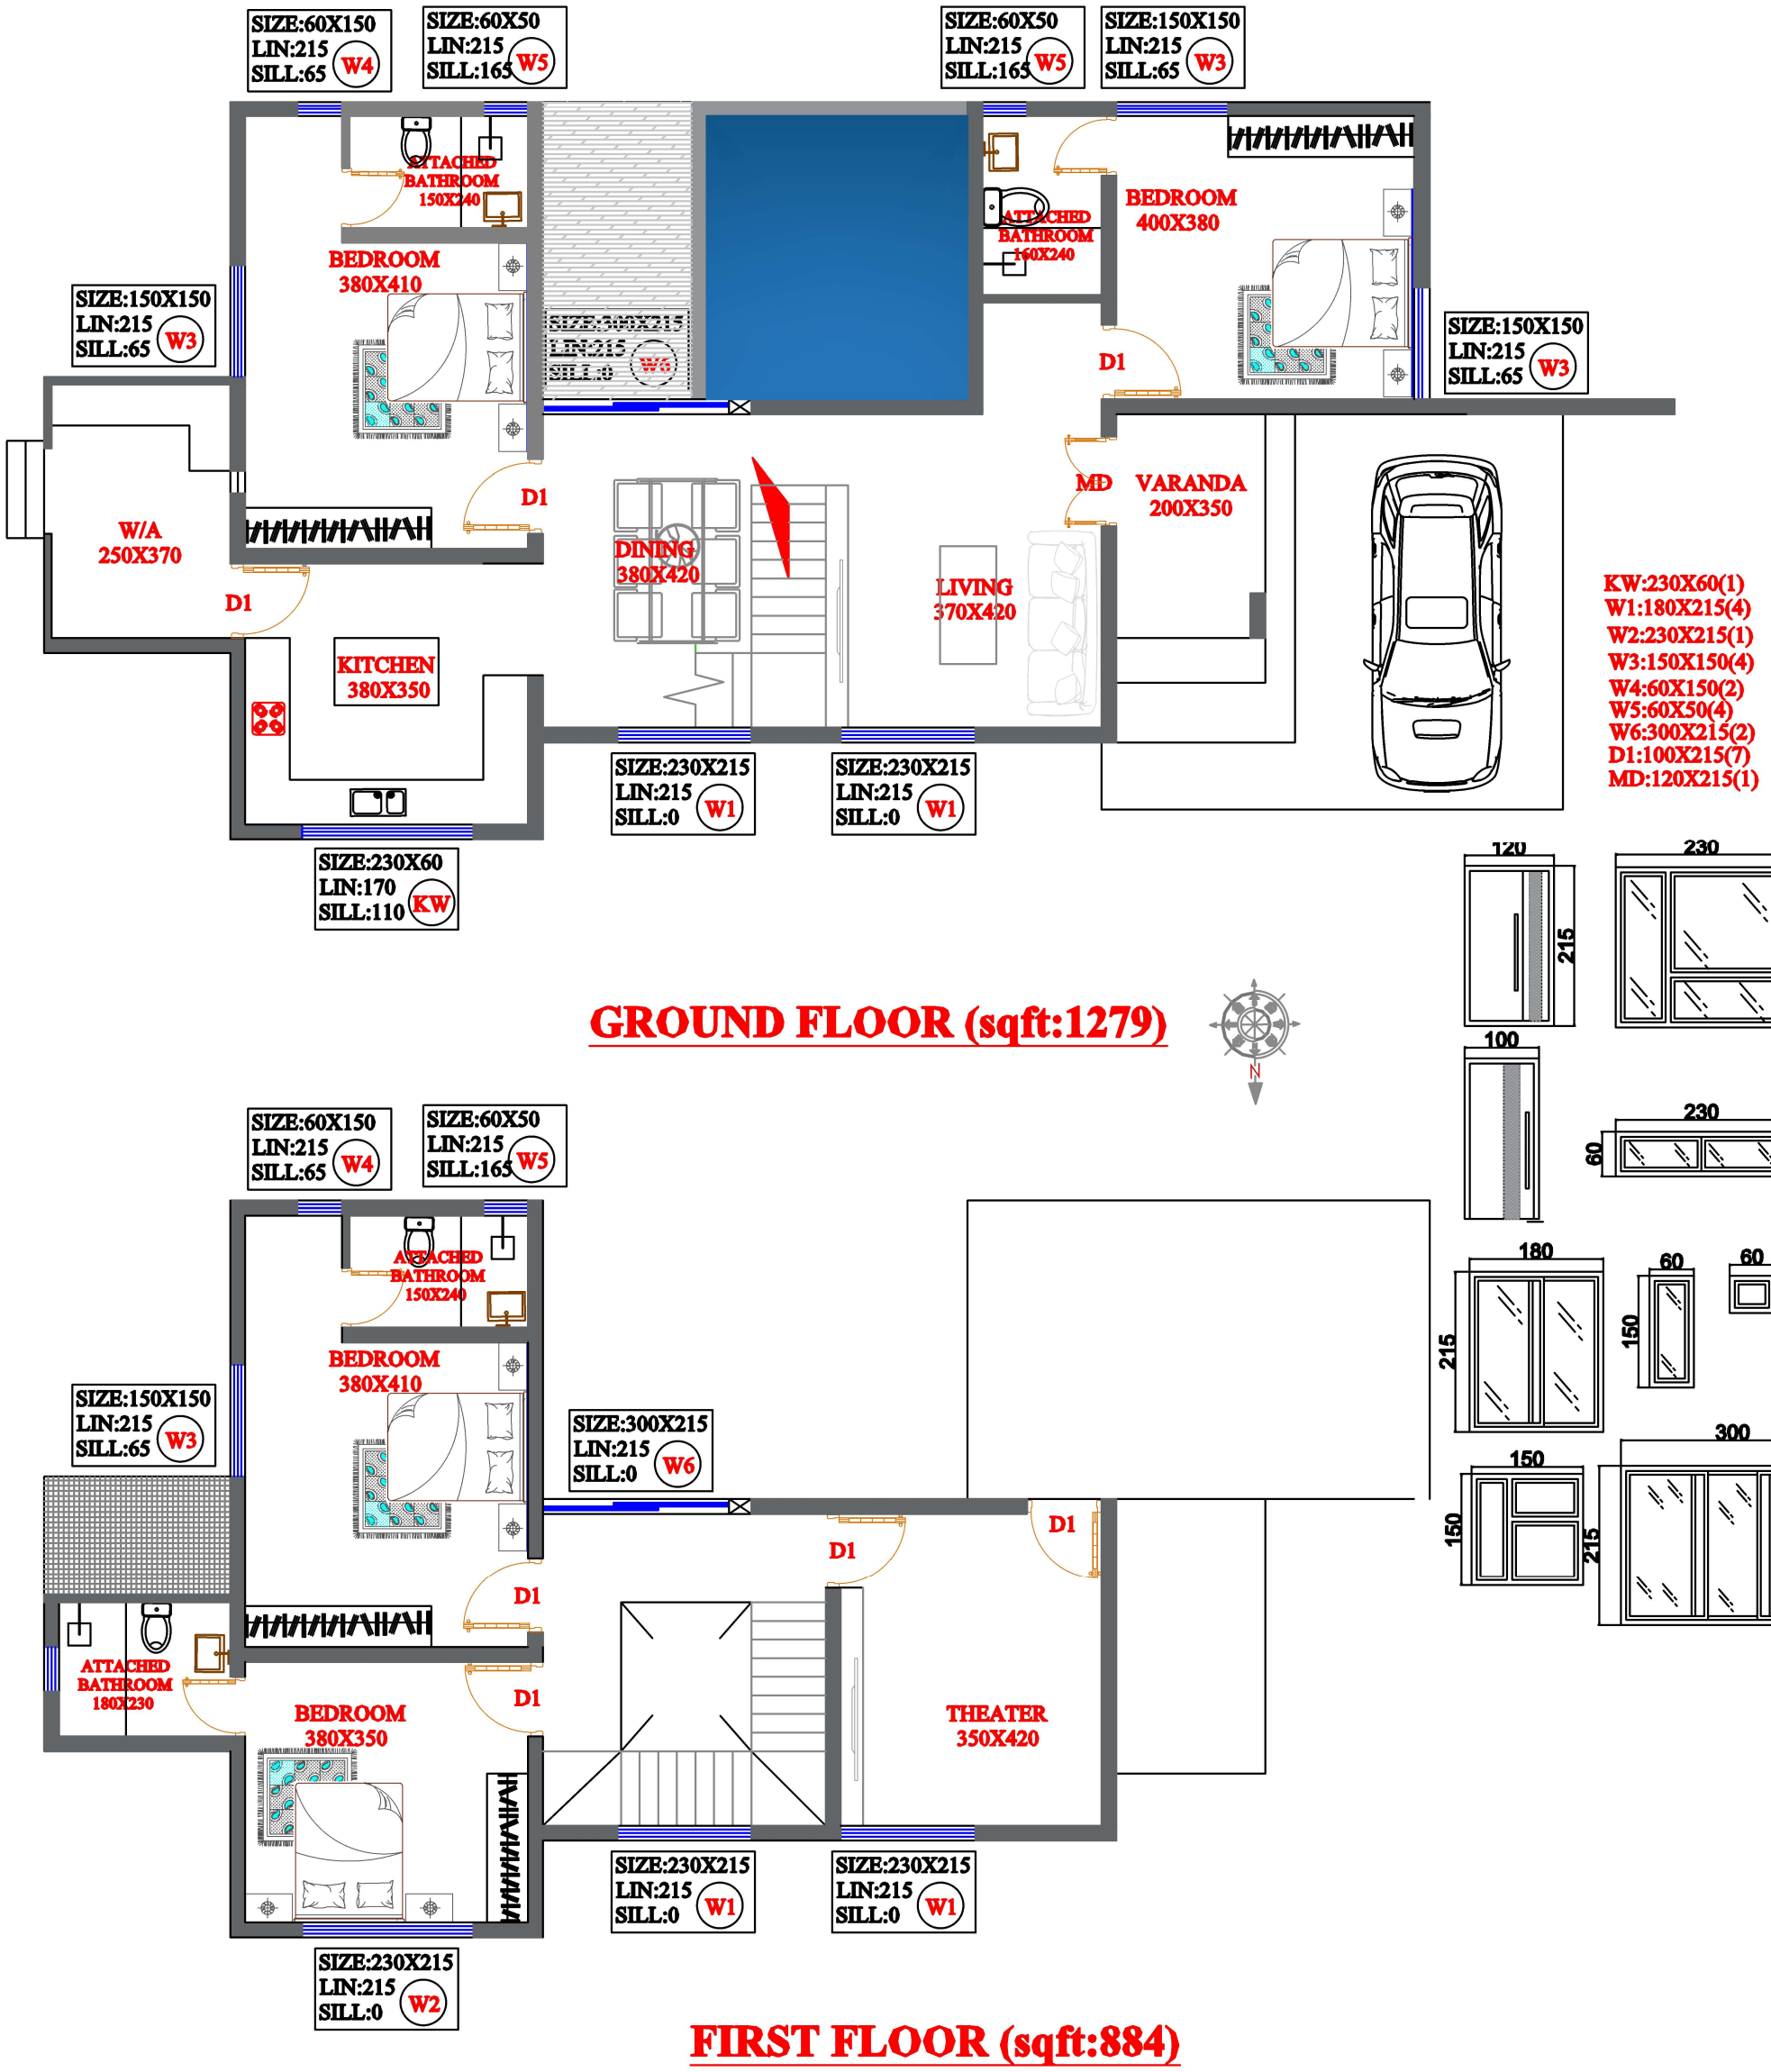


GROUND FLOOR (sqft:1279)

FIRST FLOOR (sqft:884)



SIZE:60X150
LIN:215
SILL:65
W4
SIZE:60X50
LIN:215
SILL:165
W5
SIZE:60X50
LIN:215
SILL:165
W5
SIZE:150X150
LIN:215
SILL:65
W3
ATTACHED BATHROOM 150X240
BEDROOM 380X410
ATTACHED BATHROOM 160X240
BEDROOM 400X380
SIZE:150X150
LIN:215
SILL:65
W3
SIZE:300X215
LIN:215
SILL:0
W6
D1
D1
MD
VARANDA 200X350
W/A 250X370
D1
DINING 380X420
LIVING 370X420
KITCHEN 380X350
SIZE:230X215
LIN:215
SILL:0
W1
SIZE:230X215
LIN:215
SILL:0
W1
SIZE:230X60
LIN:170
SILL:110
KW
KW:230X60(1)
W1:180X215(4)
W2:230X215(1)
W3:150X150(4)
W4:60X150(2)
W5:60X50(4)
W6:300X215(2)
D1:100X215(7)
MD:120X215(1)
GROUND FLOOR (sqft:1279)
SIZE:60X150
LIN:215
SILL:65
W4
SIZE:60X50
LIN:215
SILL:165
W5
ATTACHED BATHROOM 150X240
BEDROOM 380X410
SIZE:150X150
LIN:215
SILL:65
W3
SIZE:300X215
LIN:215
SILL:0
W6
D1
D1
D1
D1
ATTACHED BATHROOM 180X230
BEDROOM 380X350
THEATER 350X420
SIZE:230X215
LIN:215
SILL:0
W1
SIZE:230X215
LIN:215
SILL:0
W1
SIZE:230X215
LIN:215
SILL:0
W2
FIRST FLOOR (sqft:884)

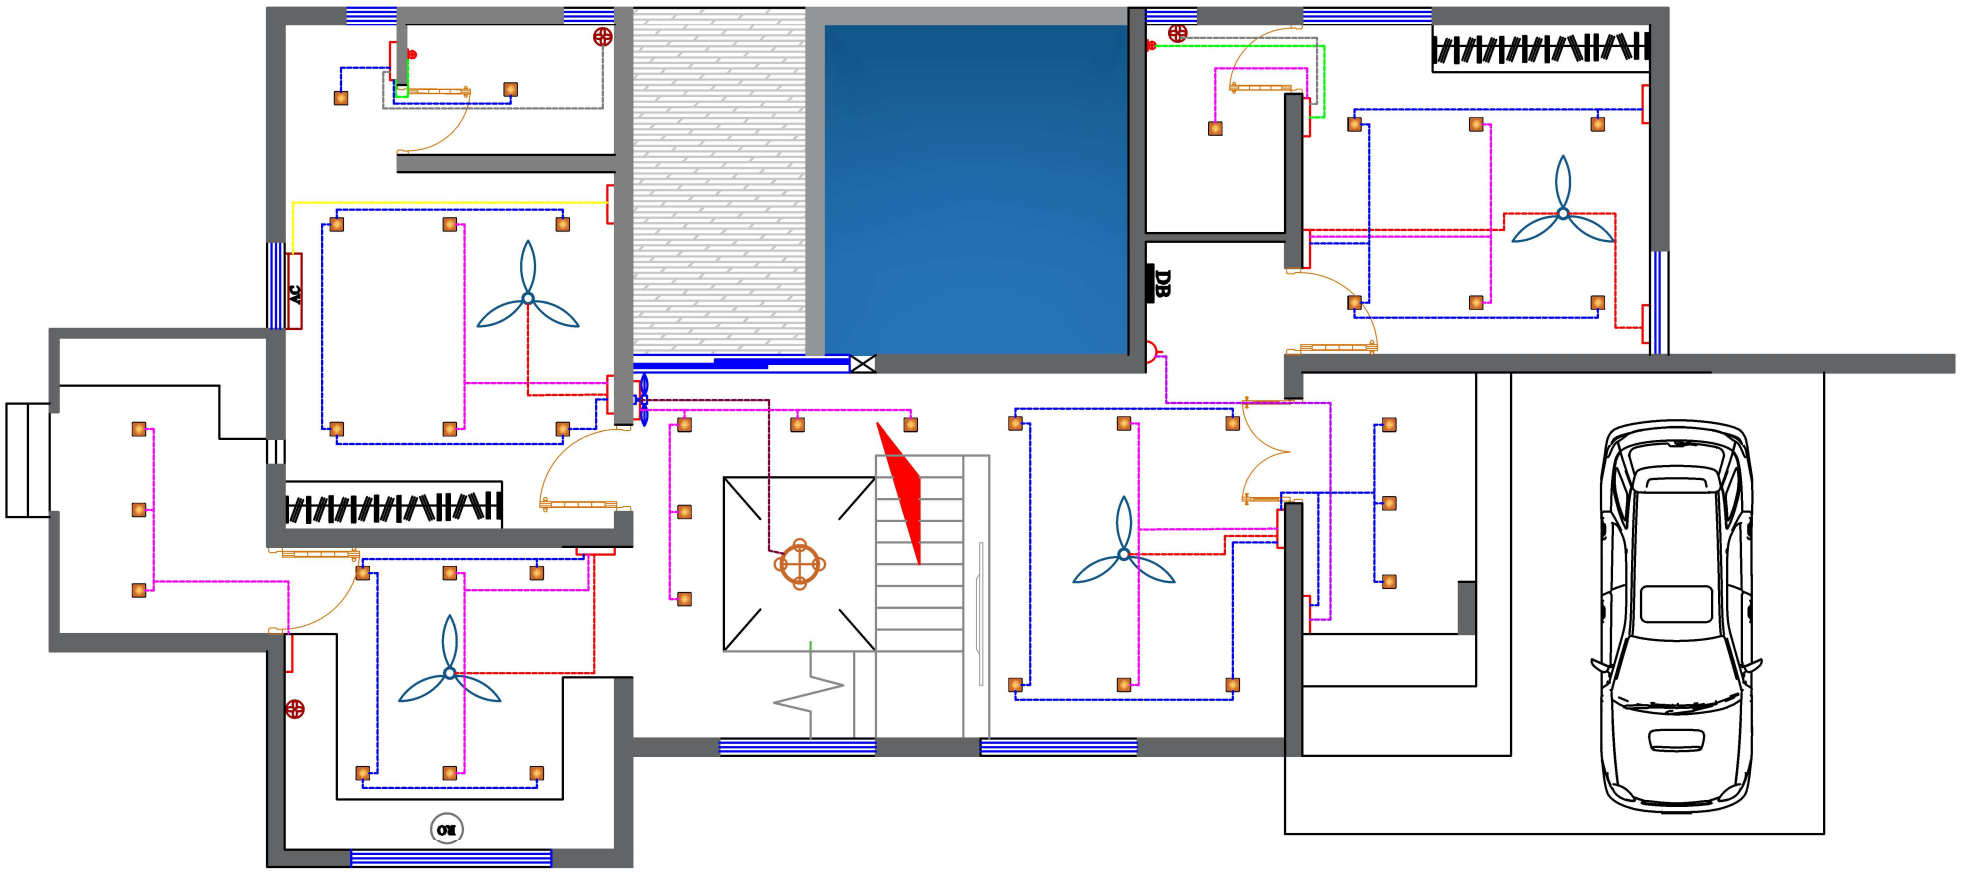


GROUND FLOOR (sqft:1279)

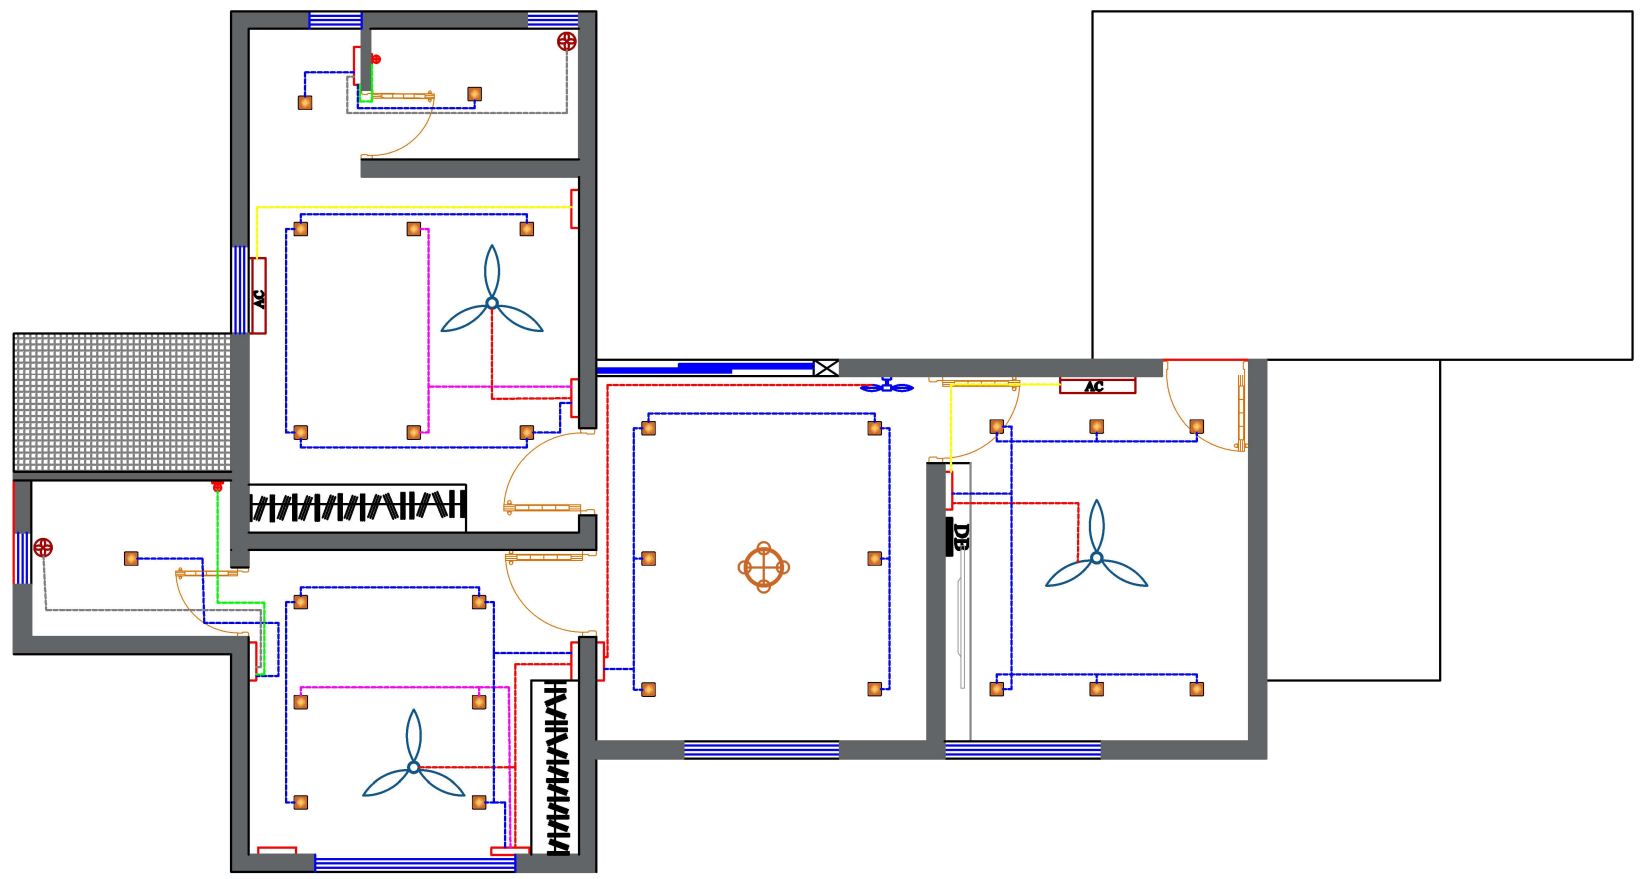

FIRST FLOOR (sqft:884)

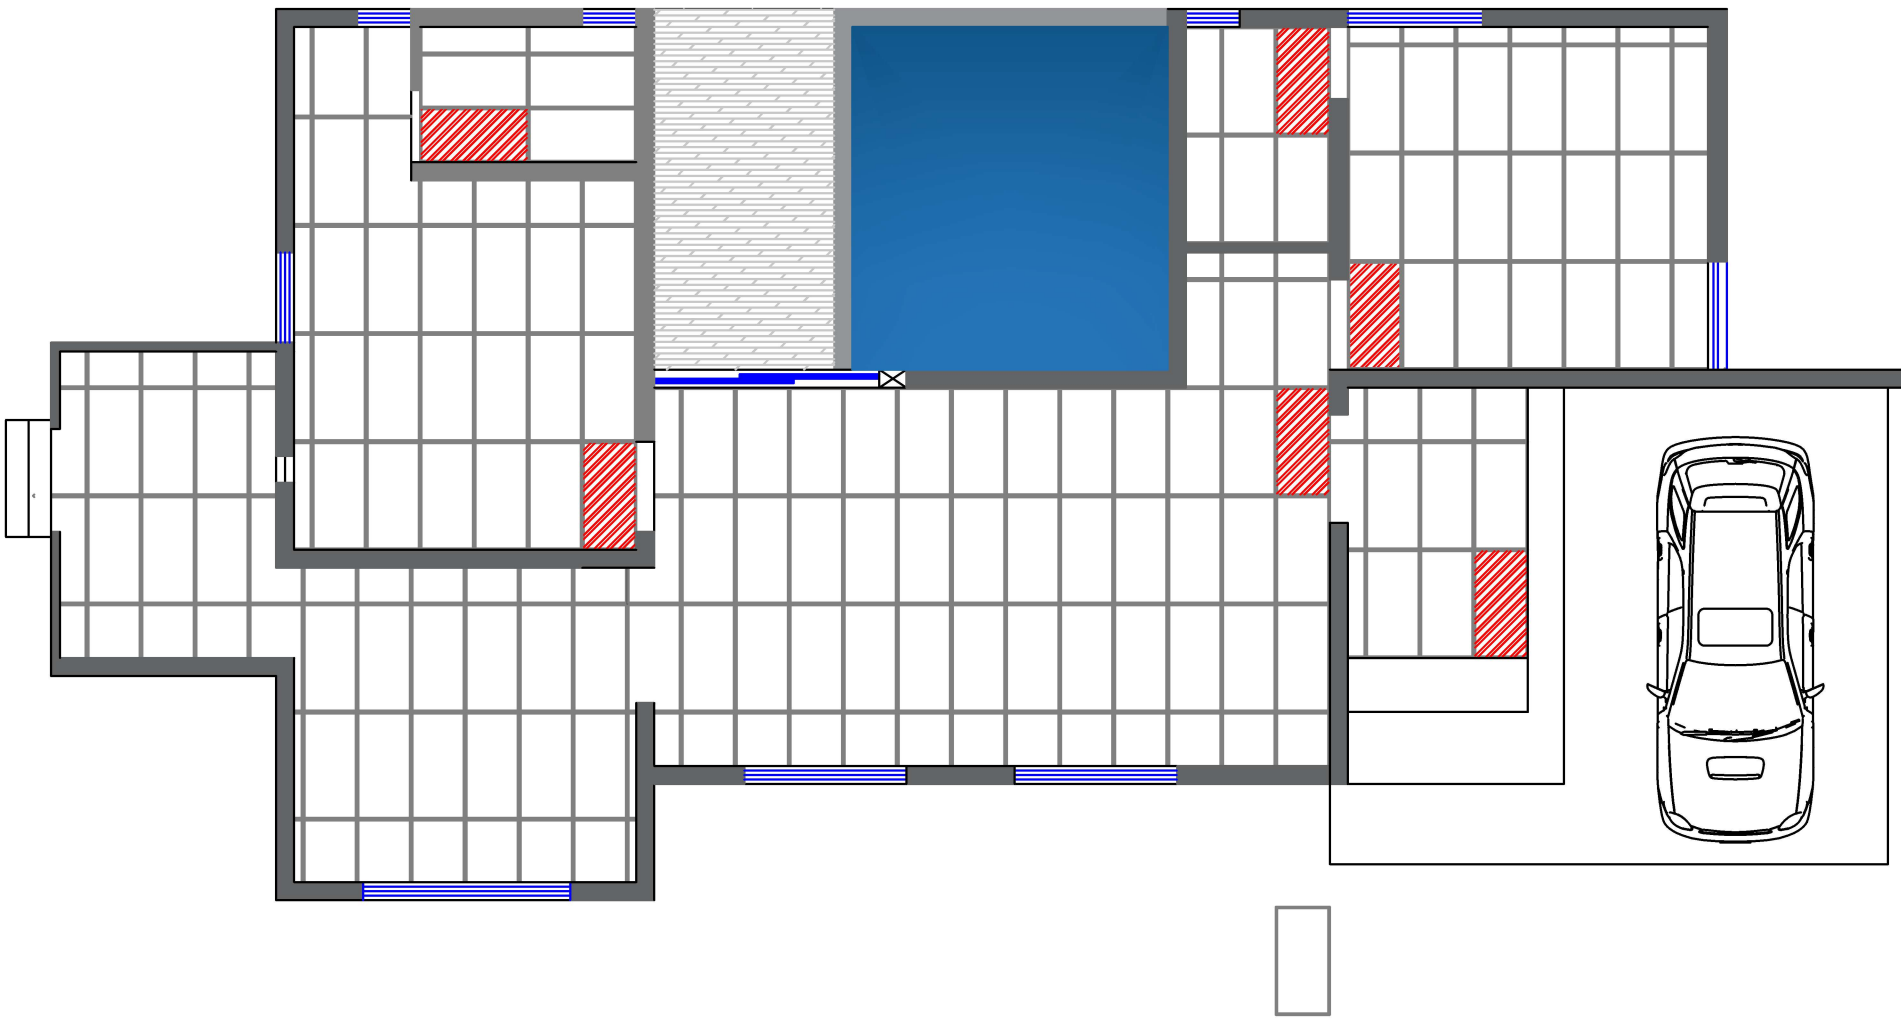

GROUND FLOOR (sqft:1279)

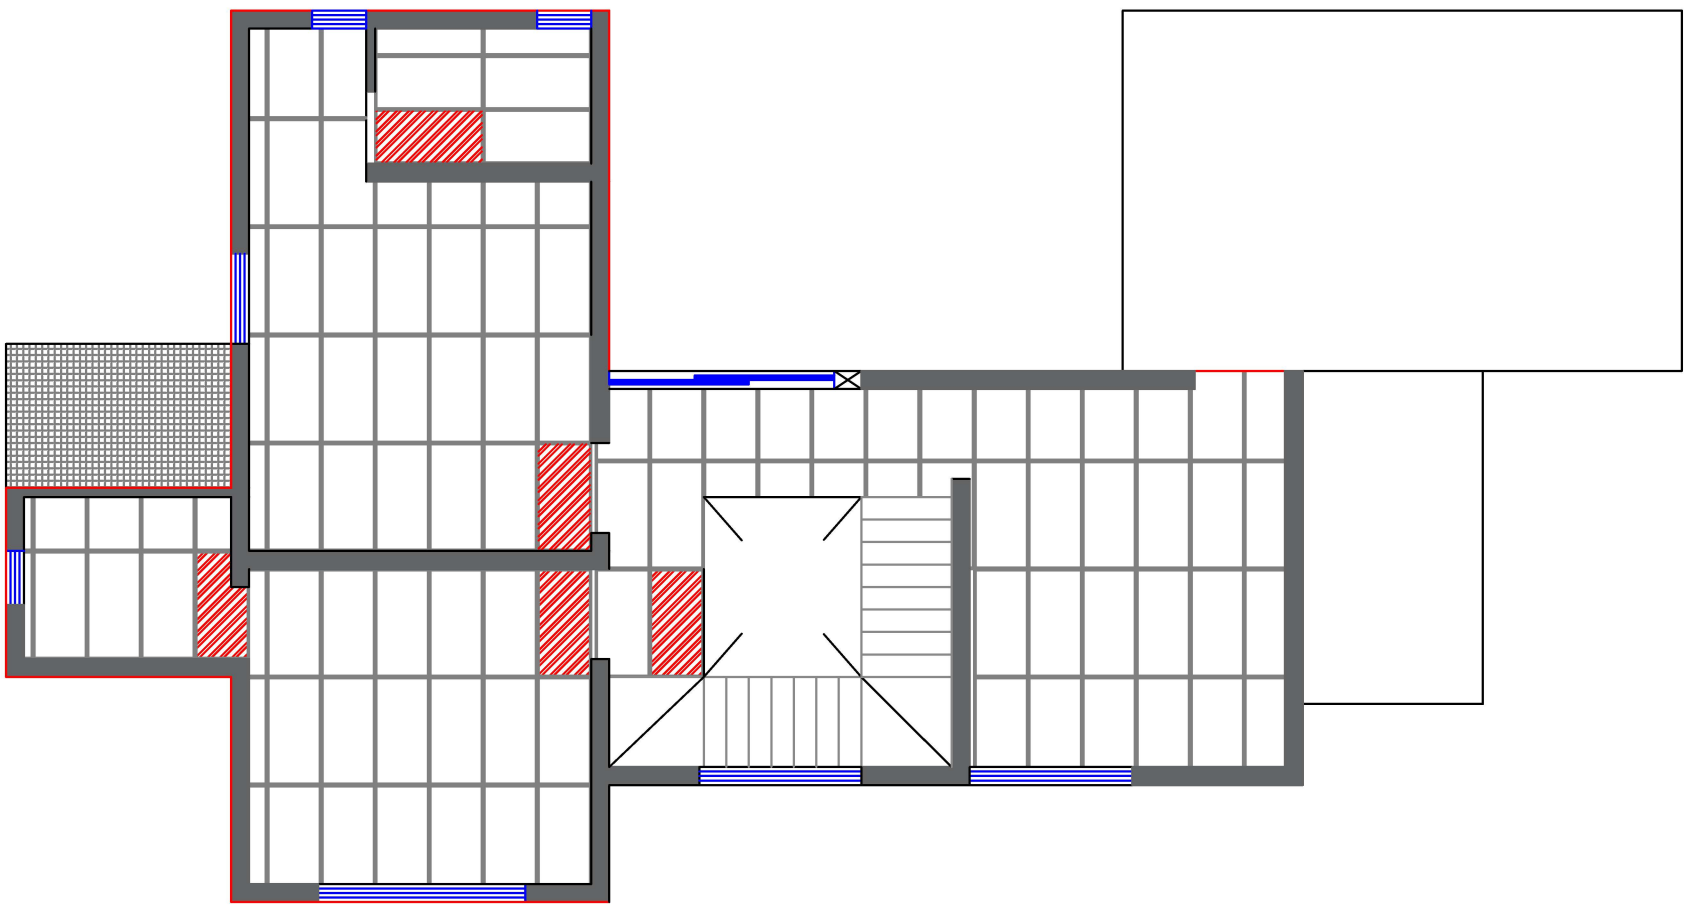

FIRST FLOOR (sqft:884)